BOVENAANZICHT, SCHAAL 1:2000

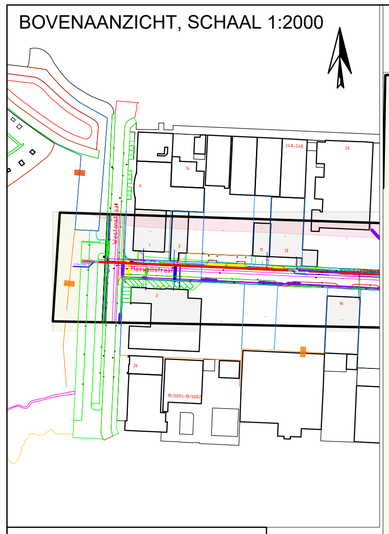

SITUATIE, SCHAAL 1:250

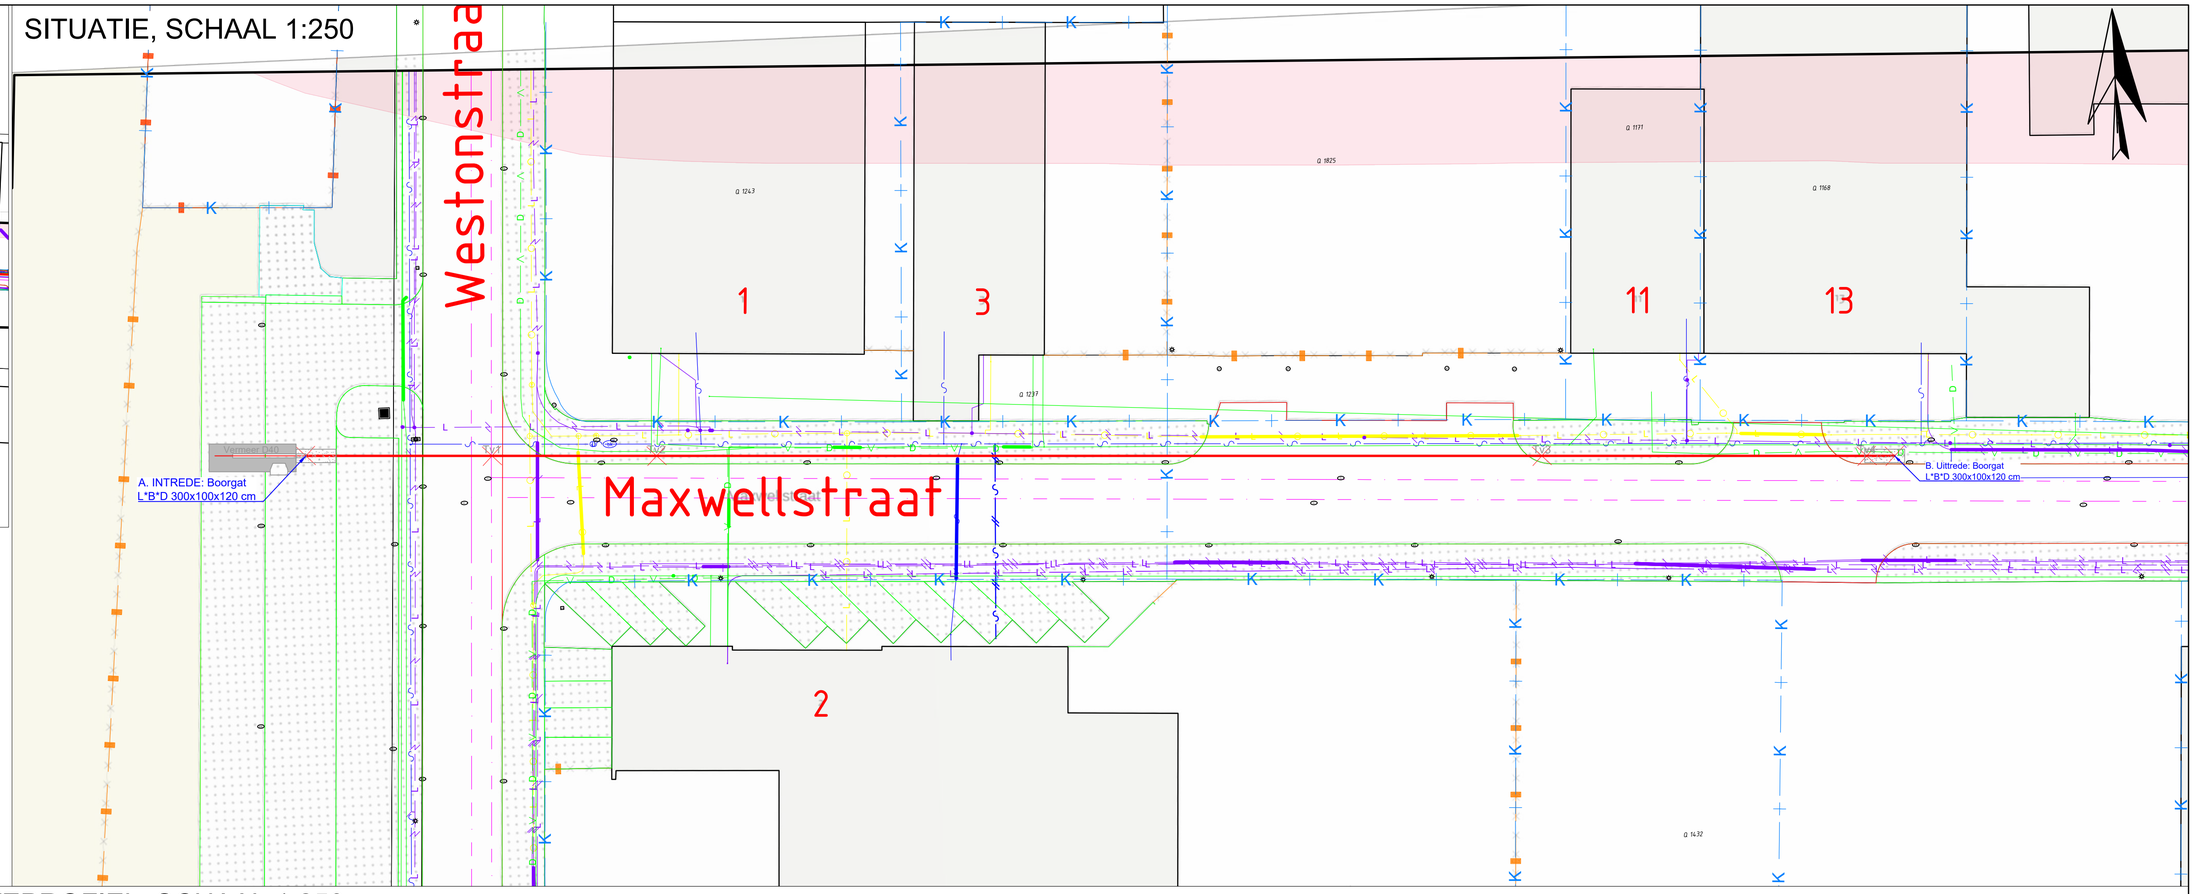

GPS PUNTEN BOORLIJN:

A: 99737.9, 496575.2
Tv1: 99751.9, 496574.6
Tv2: 99764.2, 496574.1
Tv3: 99830.7, 496571.1
Tv4: 99855, 496570
B: 99857.1, 496570
Intredehoek 18° (~ 32%)
Uittredehoek 24° (~ 45%)

DOORSNEDE BOORGAT, NoS

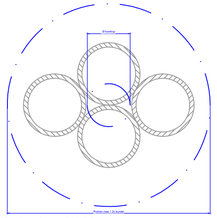

Pilotboring Ø110 mm
Ruimen Ø520 mm
Aanbrengen 4x Ø160 PE100 SDR11

LENGTEPROFIEL, SCHAAL 1:250

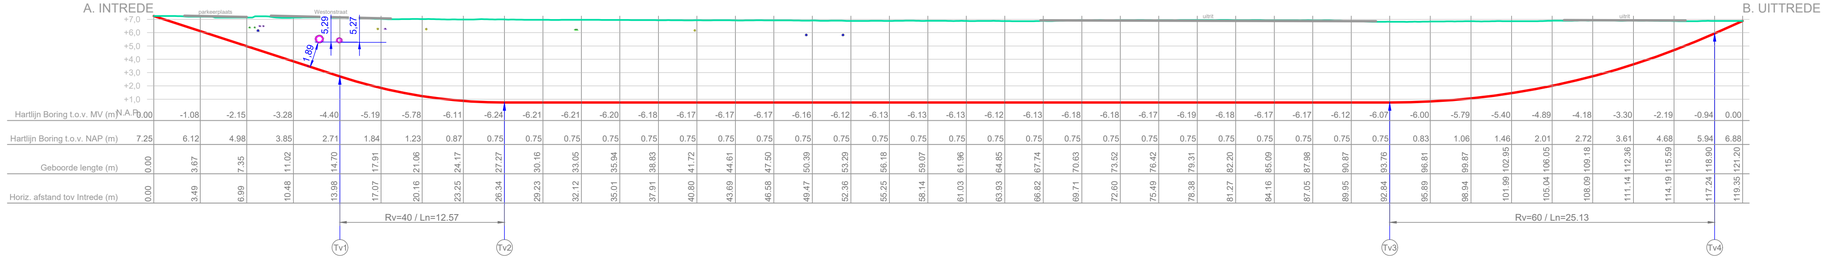

Hartlijn Boring t.o.v. MV (m)	N.A.P.	0.00	-1.08	-2.15	-3.28	-4.40	-5.19	-5.78	-6.11	-6.24	-6.21	-6.21	-6.20	-6.18	-6.17	-6.17	-6.17	-6.16	-6.12	-6.13	-6.13	-6.13	-6.12	-6.13	-6.18	-6.18	-6.17	-6.19	-6.18	-6.17	-6.17	-6.12	-6.07	-6.00	-5.79	-5.40	-4.89	-4.18	-3.30	-2.19	-0.94	0.00
Hartlijn Boring t.o.v. NAP (m)	7.25	6.12	4.98	3.85	2.71	1.84	1.23	0.87	0.75	0.75	0.75	0.75	0.75	0.75	0.75	0.75	0.75	0.75	0.75	0.75	0.75	0.75	0.75	0.75	0.75	0.75	0.75	0.75	0.75	0.75	0.75	0.75	0.75	0.83	1.06	1.46	2.01	2.72	3.61	4.68	5.94	6.88
Geboorde lengte (m)	0.00	3.67	7.35	11.02	14.70	17.91	21.06	24.17	27.27	30.16	33.05	35.94	38.83	41.72	44.61	47.50	50.39	53.29	56.18	59.07	61.96	64.85	67.74	70.63	73.52	76.42	79.31	82.20	85.09	87.98	90.87	93.76	96.81	99.87	102.95	106.05	109.18	112.36	115.59	118.90	121.20
Horiz. afstand tov Intrede (m)	0.00	3.49	6.99	10.48	13.98	17.07	20.16	23.25	26.34	29.23	32.12	35.01	37.91	40.80	43.69	46.58	49.47	52.36	55.25	58.14	61.03	63.93	66.82	69.71	72.60	75.49	78.38	81.27	84.16	87.05	89.95	92.84	95.89	98.94	101.99	105.04	108.09	111.14	114.19	117.24	119.35

LEGENDA

LIJNTYPE	OMSCHRIJVING
	BOORLIJN
	MAAIVELD
	MAATVOERING
	KADASTER
	DATA
	WATERLEIDING
	LAAGSPANNING
	RIOOL-AFVALWATER
	LEIDING

OPMERKINGEN

Diepte en ligging kabels en leidingen zijn indicatief geprojecteerd op basis van KLIC-melding. Exacte diepte en ligging vooraf controleren middels proefsleuven en visuele inspectie van (riool)putten. Diepte te passeren persleidingen onbekend. Verkeersmaatregelen treffen conform CROW publicatie 96b. Pilotboring realiseren met walk-over meetsysteem.

Rev.	Datum	Getekend	Akkoord	WIJZIGING
4				
3				
2				
1				

GestuurdeBoringTekening.nl

3D-DRILLING BV

IN OPDRACHT VAN:
Liander
-
Postbus 50
6920 AB Duiven

PROJECT: HDD7&8 IJmuiden, Maxwellstraat
4x Ø160 PE100 SDR11
Geboorde lengte 121.2 m

ONDERWERP: Gestuurde boring

ORDERNR.:	3D25V640
GETEKEND:	M.Luijben
AKKOORD :	M.Visser
DATUM :	18-jul-25
SCHAAL :	1:250
FORMAAT :	A2Z1

STATUS: Vergunning

TEKENING NR.: 3D25V640-03

REV. 0